


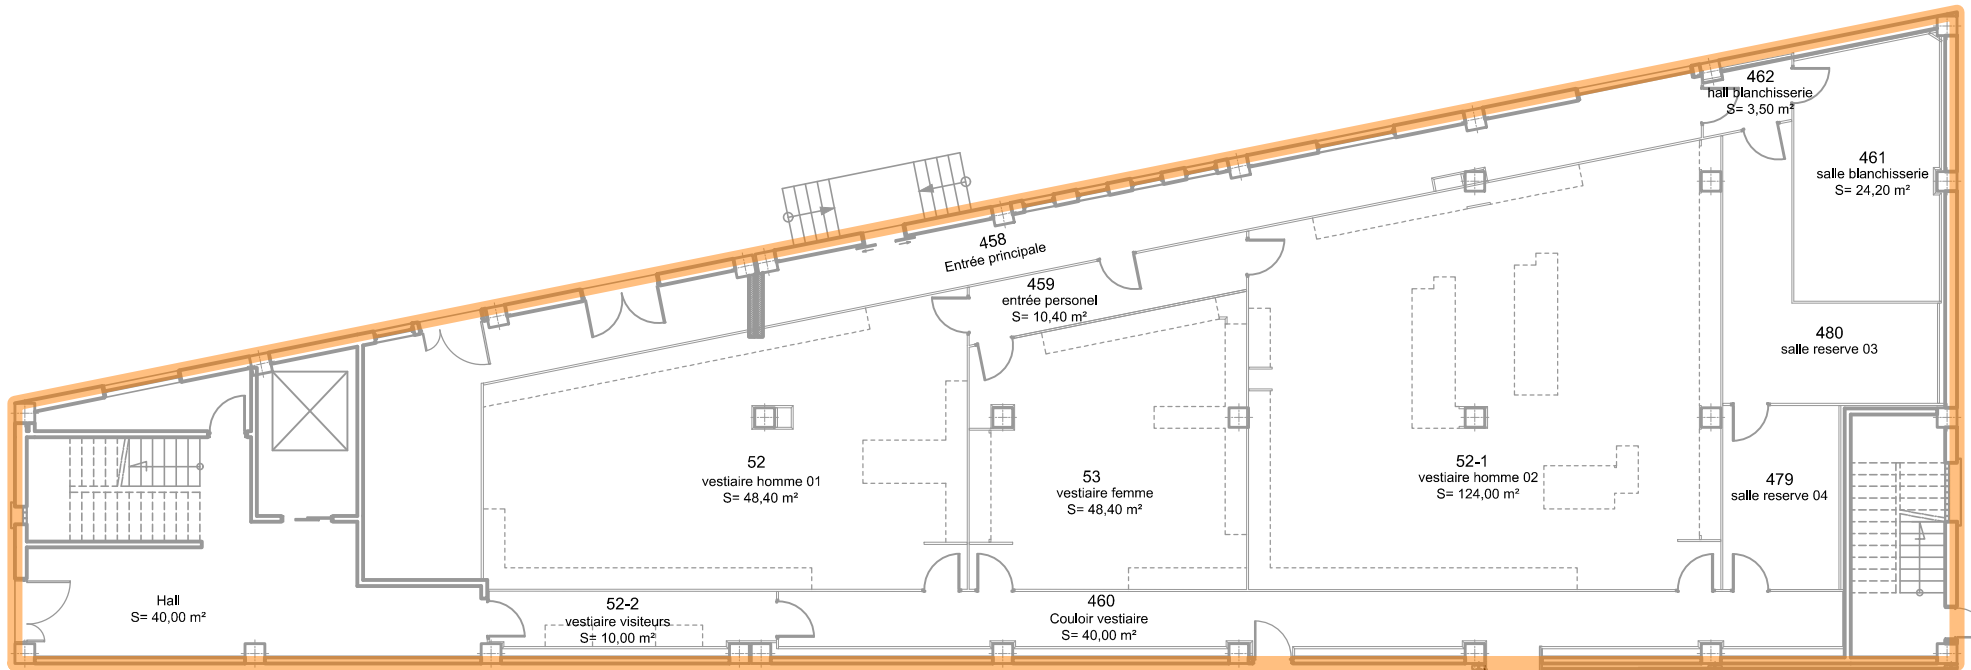

LEGENDE :

- BANDES SEPARATION ZONES
- TRANSFERT MATIERES PREMIERES
- RECEPTION A.C PRIMAIRE ET SECONDAIRE
- LIVRAISON PRODUITS FINIS
- FLUX ARTICLE DE CONDITIONNEMENT SECONDAIRES
- FLUX ARTICLES DE CONDITIONNEMENT PRIMAIRES
- FLUX VRAC & INTERMEDIAIRES
- FLUX PRODUITS FINIS
- FLUX MATIERES PREMIERES
- FLUX SF DES PRODUITS PHARMACEUTIQUES SOUS FORME DE SOLUTION INJECTABLE


ZONE DE PRODUCTION DES FORMES SECHES

ZONE DE PRODUCTION DES FORMES SEMI-SOLIDES

ZONE DE CONDITIONNEMENT SECONDAIRE DES PRODUITS PHARMACETIQUES BIOLOGIQUES SOUS FORME INJECTABLE

ZONE DE PESEE

VESTIAIRES

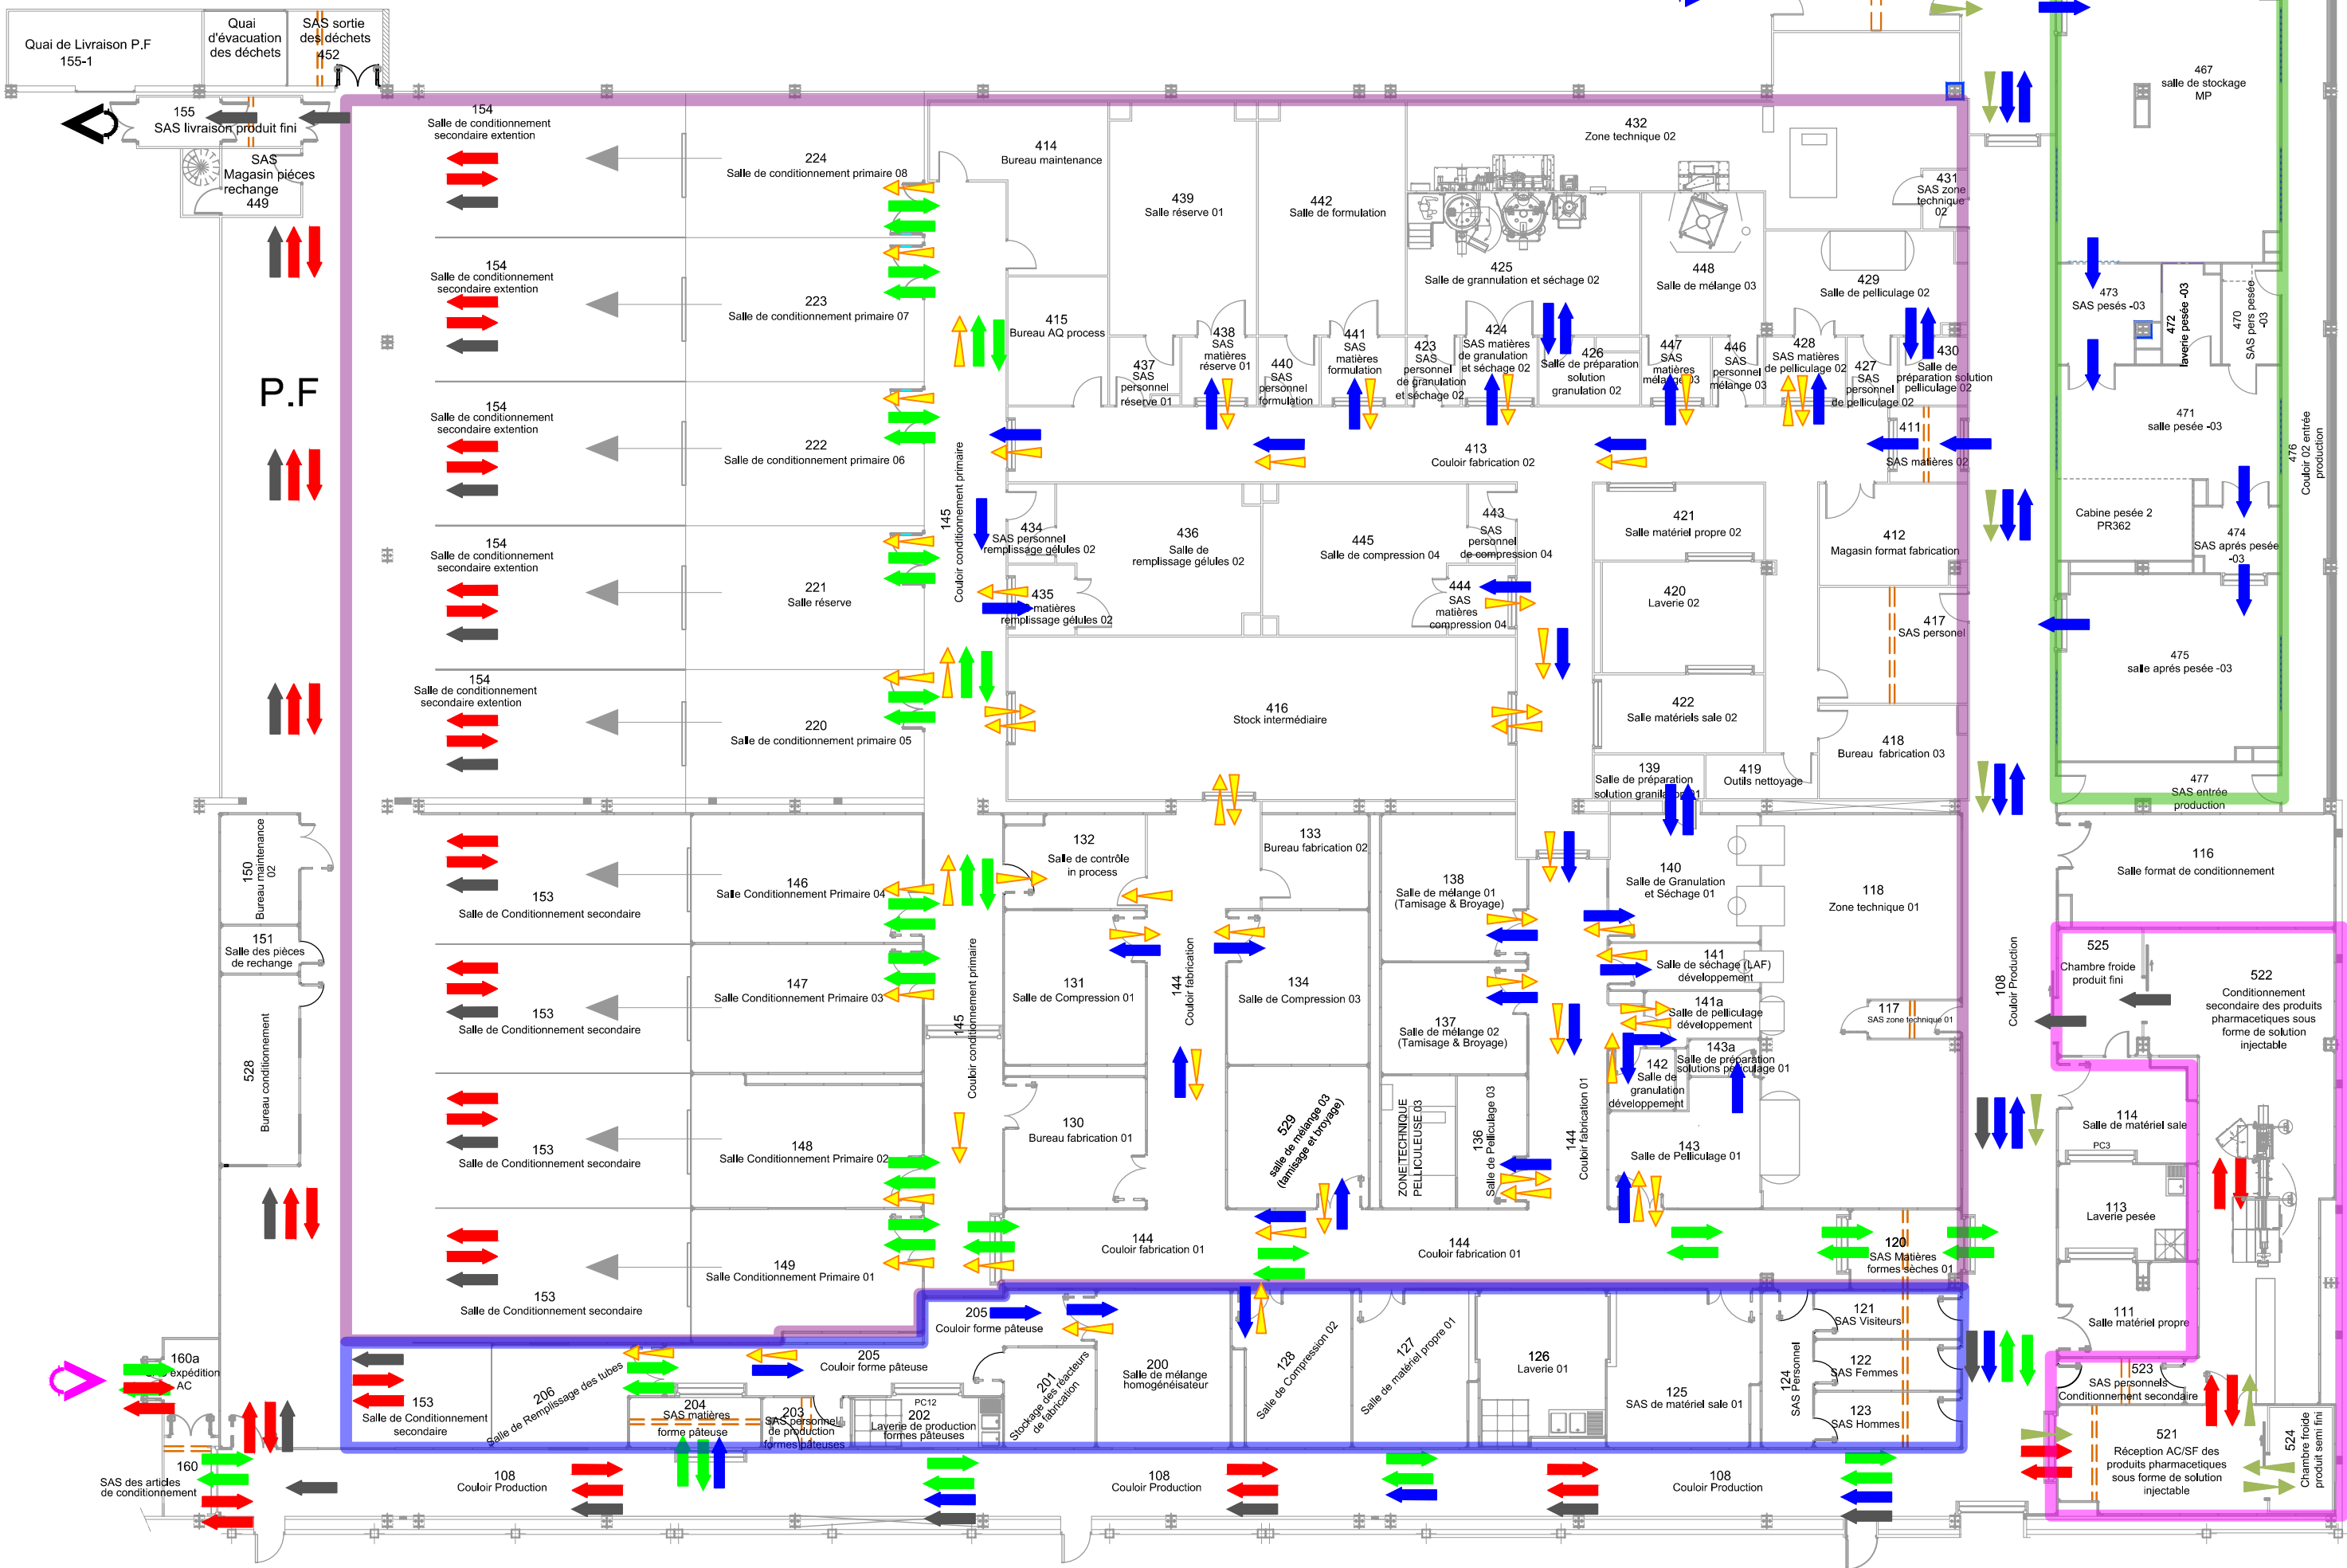

TITRE :
**FLUX PRODUITS ZONE
PRODUCTION**

REFERENCE / VERSION : P027 / V11

DESSINE PAR :Omar HAMMADA

APPROBATION (date & visa)

PROPRIETAIRE DU SYSTEME

AQ

DT

DS